




THIẾT BỊ ĐO LƯU LƯỢNG KẾT HỢP NHIỆT ĐỘ VÀ ÁP SUẤT KHÍ THẢI

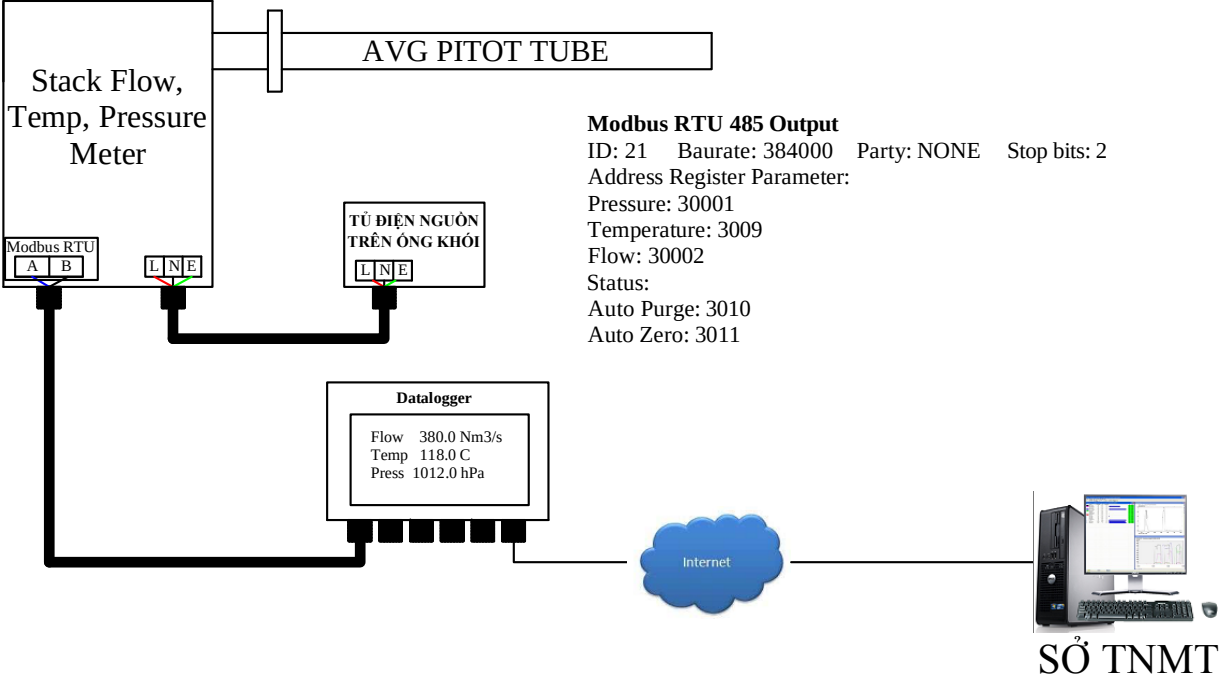


THIẾT BỊ PHÂN TÍCH KHÍ THẢI O2, CO, NO, NO2, SO2

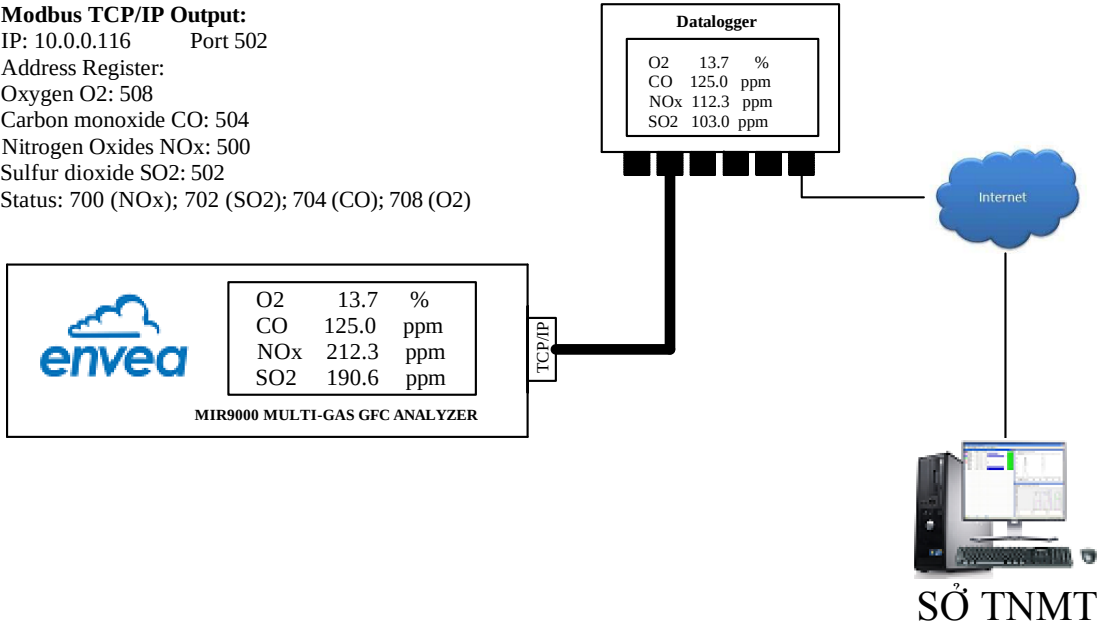

THIẾT BỊ ĐO BỤI TỔNG PM

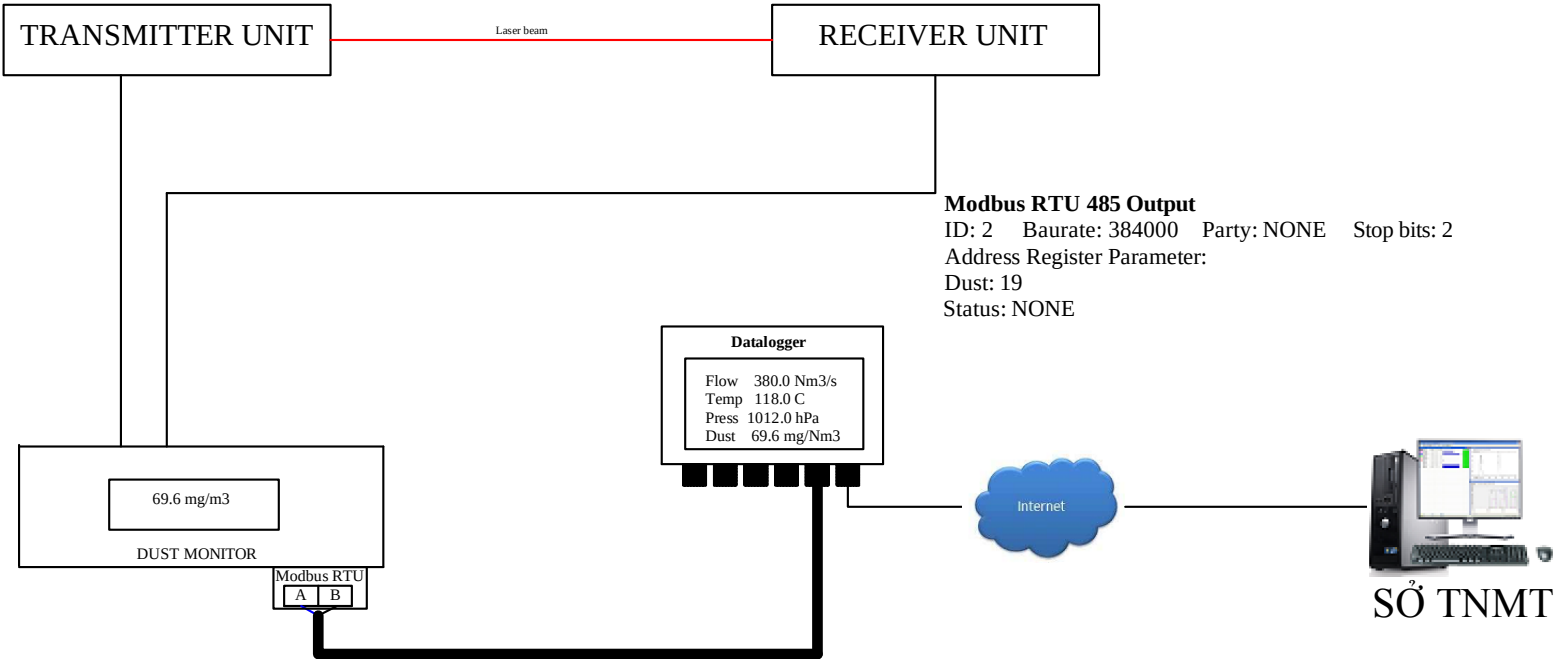

CAMERA GIÁM SÁT

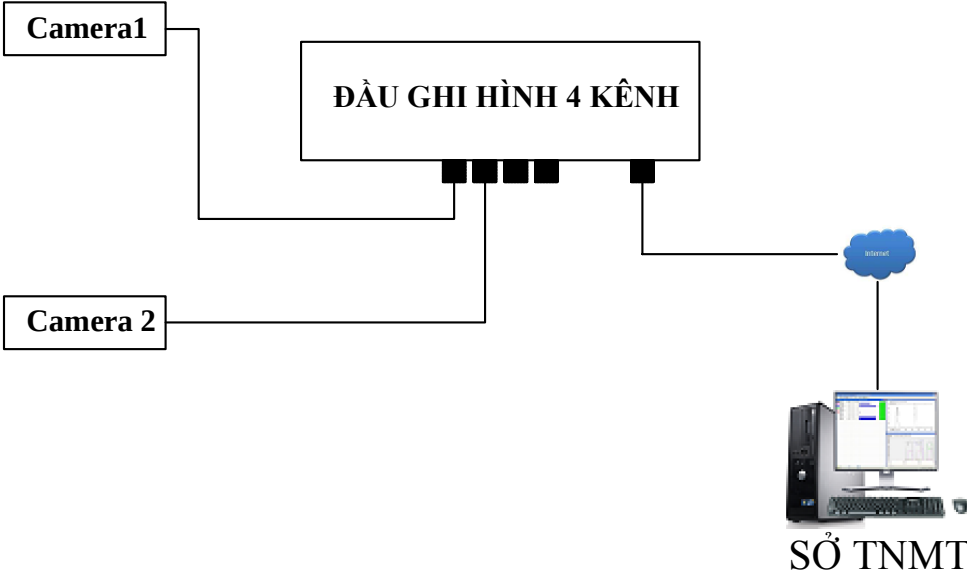

	Họ và tên	Chữ ký	SƠ ĐỒ KẾT NỐI TÍN HIỆU TRẠM QUAN TRẮC KHÍ THẢI TỰ ĐỘNG		
Duyệt			Ngày thiết kế	Tỷ lệ	Số hiệu bản vẽ
Thiết kế			10 - 02 - 2020	 /	CT02/HV.2019
Kiểm tra					